This copy is a controlled copy only if it so stamped in red ink

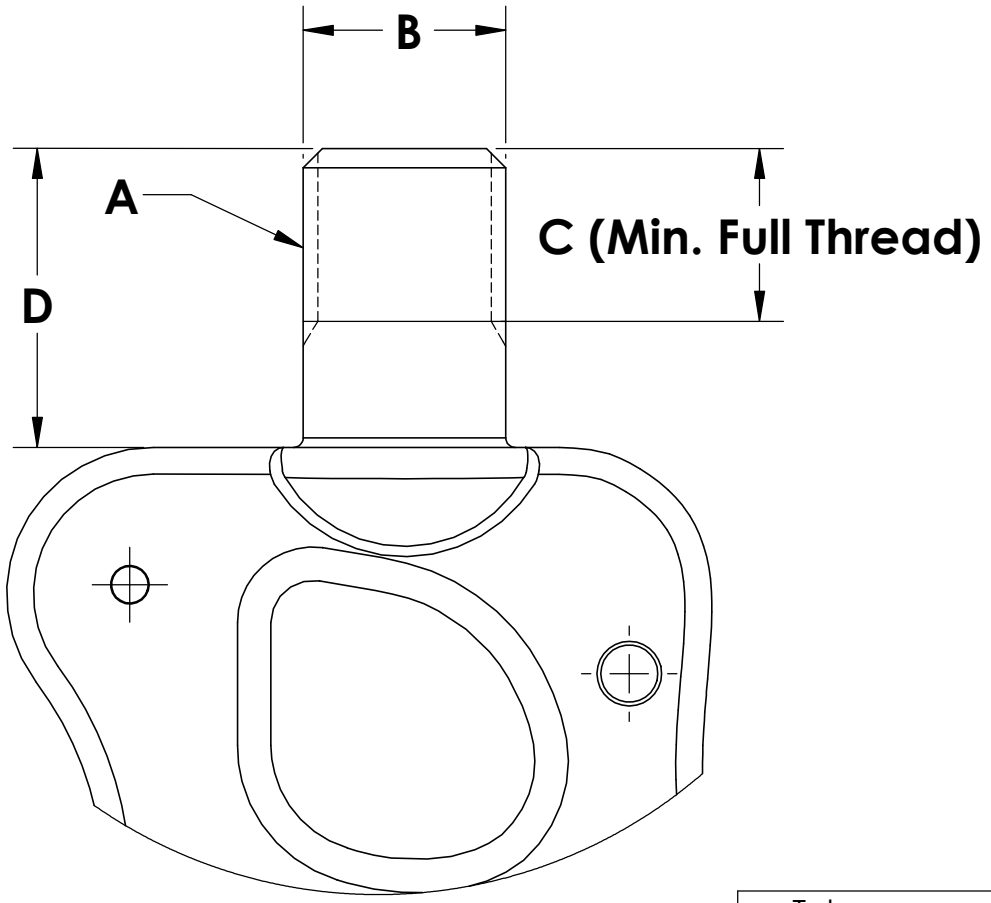

	A	B	C	D
T5	M10x1.5 - 6g	.388 ±.004	0.290	0.480
T8	M10x1.5 - 6g	.388 ±.004	0.310	0.560
T12	M12x1.75 - 6g	0.466	0.330	0.635
T16	M14x2 - 6g	0.545	0.440	0.760 ±.010
T20	M16x2 - 6g	0.623	0.480	0.800 ±.010
T30	M20x2.5 - 6g	0.780	0.580	1.060 ±.010
T40	M27x3 - 6g	1.055	0.900	1.555 ±.015
T50	M30x3.5 - 6g	1.174	0.940	1.750 ±.015

PROPRIETARY AND CONFIDENTIAL

THE INFORMATION CONTAINED IN THIS DRAWING IS THE SOLE PROPERTY OF VECTOR ENGINEERING INC. ANY REPRODUCTION IN PART OR AS A WHOLE WITHOUT THE WRITTEN PERMISSION OF VECTOR ENGINEERING INC. IS PROHIBITED.

Tolerances Unless Specified

Decimal: +/- .005

Fractional: +/- $\frac{1}{64}$

Angular: +/- 1 deg.

Units: Inches [Millimeters]

Tylaska Marine & Aerospace
DBA Vector Engineering
800 Flanders Rd
Mystic, CT 06355
Tel: (860)-572-8440
Fax: (860)-572-0534
Email: Tim@Tylaska.com

Thomas Dixon

8/15/2017

Material: 17-4 PH SS

T-Shackle Shank Threads and Dimensions

SIZE **A** | DWG. NO. T-Shackle Threads | REV F

SCALE: 1:1 | WI 7.7-5 | SHEET 1 OF 1

5 4 3 2 1